

BQ 815083 ✓

DAFTAR ISIAN 206

BADAN PERTANAHAN NASIONAL REPUBLIK INDONESIA



SERTIPIKAT (TANDA BUKTI HAK)

KANTOR PERTANAHAN
KABUPATEN / KOTA

ADMINISTRASI JAKARTA PUSAT

09 • 01 • 07 • 02 • 3 • 03649

BADAN PERTANAHAN NASIONAL REPUBLIK INDONESIA



BUKU TANAH

GUNA BANGUNAN

No. 3649

PROVINSI :

KABUPATEN / KOTA :

KECAMATAN :

DESA / KELURAHAN :

KANTOR PERTANAHAN
KABUPATEN / KOTA

ADMINISTRASI JAKARTA PUSAT

DAERAH KHUSUS IBUKOTA JAKARTA

ADMINISTRASI JAKARTA PUSAT

CEMPAKA PUTIH

CEMPAKA PUTIH TIMUR.

DAFTAR ISIAN 307

No. —

DAFTAR ISIAN 208

No. 2585 /P / 2017

09 • 01 • 07 • 02 • 3 • 03649

PENDAFTARAN - PERTAMA

Halaman :

<p>a) HAK : GUNA BANGUNAN No. : 3649 Desa / Kel. : CEMPAKA PUTIH TIMUR Tgl. berakhirnya hak : 22/10/2033</p>	<p>i) NAMA PEMEGANG HAK -Perusahaan Terbatas "PT. KARYADEKA PANCAMORNI", berkedudukan di Jakarta Barat</p>
<p>b) NIB 09.01.07.02.05100 Letak Tanah Jalan Jenderal Ahmad Yani Kav 72-73</p>	<p>Tanggal lahir / akta pendirian Tanggal 13-08-2008, No. 51, dibuat dihadapan FATHIAH HELMI, SH, Notaris di Jakarta dan telah mendapat persetujuan dari Menteri Hukum dan Hak Asasi Manusia RI tanggal 10-11-2009 Nomor AHU 82260.41.101-01 Tahun 2009</p>
<p>c) ASAL HAK 1. Konversi 2. Pemberian hak 3. Pemecahan / Pemisahan / dari HGB No 3510/Cempaka Putih Timur Penegabungan bidang</p>	<p>g) PEMBUKUAN Jakarta, 13 - 02 - 2017</p>
<p>d) DASAR PENDAFTARAN 1. Daftar Isian 202 Tgl. No. 2. Surat Keputusan Tgl. No. 3. Permohonan Pemecahan / Pemisahan / Penggabungan bidang Tgl. No.</p>	<p>h) PENERBITAN SERTIPIKAT Jakarta, 13 - 02 - 2017</p>
<p>e) SURAT UKUR Tgl. 09/02/2017 No. 00256/Cempaka Putih Timur/2017 Luas 4719 M² (Empat ribu tujuh ratus sembilan meter persegi)</p>	<p>An. Kepala Kantor Pertanahan Kabupaten / Kota Administrasi Jakarta Pusat Kepala Seksi Hak Tanah dan Pendaftaran Tanah Kepala Sub Seksi Pendaftaran Hak ARIANTO KALTARA, SH NIP 19831222.198609.1.001</p>
<p>i) PENUNJUK Pemecahan Atas Nama Sendiri</p>	<p>An. Kepala Kantor Pertanahan Kabupaten / Kota Administrasi Jakarta Pusat Kepala Seksi Hak Tanah dan Pendaftaran Tanah Ub. Kepala Sub Seksi Pendaftaran Hak ARIANTO KALTARA, SH NIP 19831222.198609.1.001</p>

PENDAFTARAN PERALIHAN HAK, PEMBEBANAN DAN PENCATATAN LAINNYA

Halaman :

<p>Sebab perubahan, Tanggal pendaftaran, No. Daftar isian</p> <p>JUAL-BELI</p> <p>Akta PPAT, MARINA SOEWANA, Sarjana Hukum Tgl. 07/03/2017 Nomor 27/2017</p> <p>301.4026/JB / 2017</p>	<p>Nama yang berhak dan Pemegang hak lainnya</p> <p>Telah Meminta Pengecekan Sertifikat Daftar Isian. 303 No. : 3002</p> <p><i>M. Marina - SH</i></p>	<p>Tanda tangan Kepala Kantor dan Cap Kantor</p> <p>Perseroan Terabatas : PT. CEMPaka CITRA PERDANA Berkedudukan di Kota Cimahi.</p> <p><i>Sohar Rose</i></p> <p>An. Kepala Kantor Pertanahan Kota Administrasi Jakarta Pusat Kepala Seksi Hak Tanah dan Pendaftaran Tanah</p> <p>SUHARTA, SH. NIP. 19610413 198303 1 004</p>
<p>JUAL-BELI</p> <p>Akta PPAT, MARINA SOEWANA, Sarjana Hukum Tgl. 07/03/2017 Nomor : 27/2017</p> <p>301.4026/JB / 2017</p>		
<p>Perseroan Terabatas : PT. CEMPaka CITRA PERDANA Berkedudukan di Kota Cimahi.</p> <p><i>Sohar Rose</i></p> <p>An. Kepala Kantor Pertanahan Kota Administrasi Jakarta Pusat Kepala Seksi Hak Tanah dan Pendaftaran Tanah</p> <p>SUHARTA, SH. NIP. 19610413 198303 1 004</p>		
<p>Tgl. 16 -03-2017 No. 3940 /2017</p>		

PENDAFTARAN PERALIHAN HAK, PEMBEBANAN DAN PENCATATAN LAINNYA

Halaman :

Sebab perubahan, Tanggal pendaftaran, No. Daftar isian	Nama yang berhak dan Pemegang hak lain-lainnya	Tanda tangan Kepala Kantor dan Cap Kantor
		

BQ 815083

0 9 • 0 1 • 0 7 • 0 2 • 3 • 0 3 6 4 9

NIB : 09.01.07.02.05100

DAFTAR ISIAN 207

SURAT UKUR

Nomor : 00256 / Cempaka Putih Timur / 2017

SEBIDANG TANAH TERLETAK DALAM

Provinsi : Daerah Khusus Ibukota Jakarta

Kabupaten / Kota : Administrasi Jakarta Pusat

Kecamatan : Cempaka Putih

Desa / Kelurahan : Cempaka Putih Timur, Jalan Jenderal Ahmad Yani Kav 72-73

Peta : Nomor Peta Pendaftaran : 48.2-35.090-01-9

Lembar : Kotak :

FG DKI No. 50/30 Kotak : C-D/3-4 dan FG DKI No. 50-20-31 Kotak : C-D-E/1-4-5

Keadaan Tanah : Terdapat bangunan permanen.

Tanda-tanda batas : telah terpasang sesuai dengan PMNA/Kepala BPN No. 3 Tahun 1997.

Luas : 4.719 m² (Empat ribu tujuh ratus sembilan belas meter persegi)


Penunjukan dan penetapan batas : Batas-batas ditunjukkan oleh : Mustopa Staf PT.

Karyadeka Pancamurni

Pemohon : PT. Karyadeka Pancamurni

Diukur oleh : Yayan, SH.

SKALA 1 : 1.000

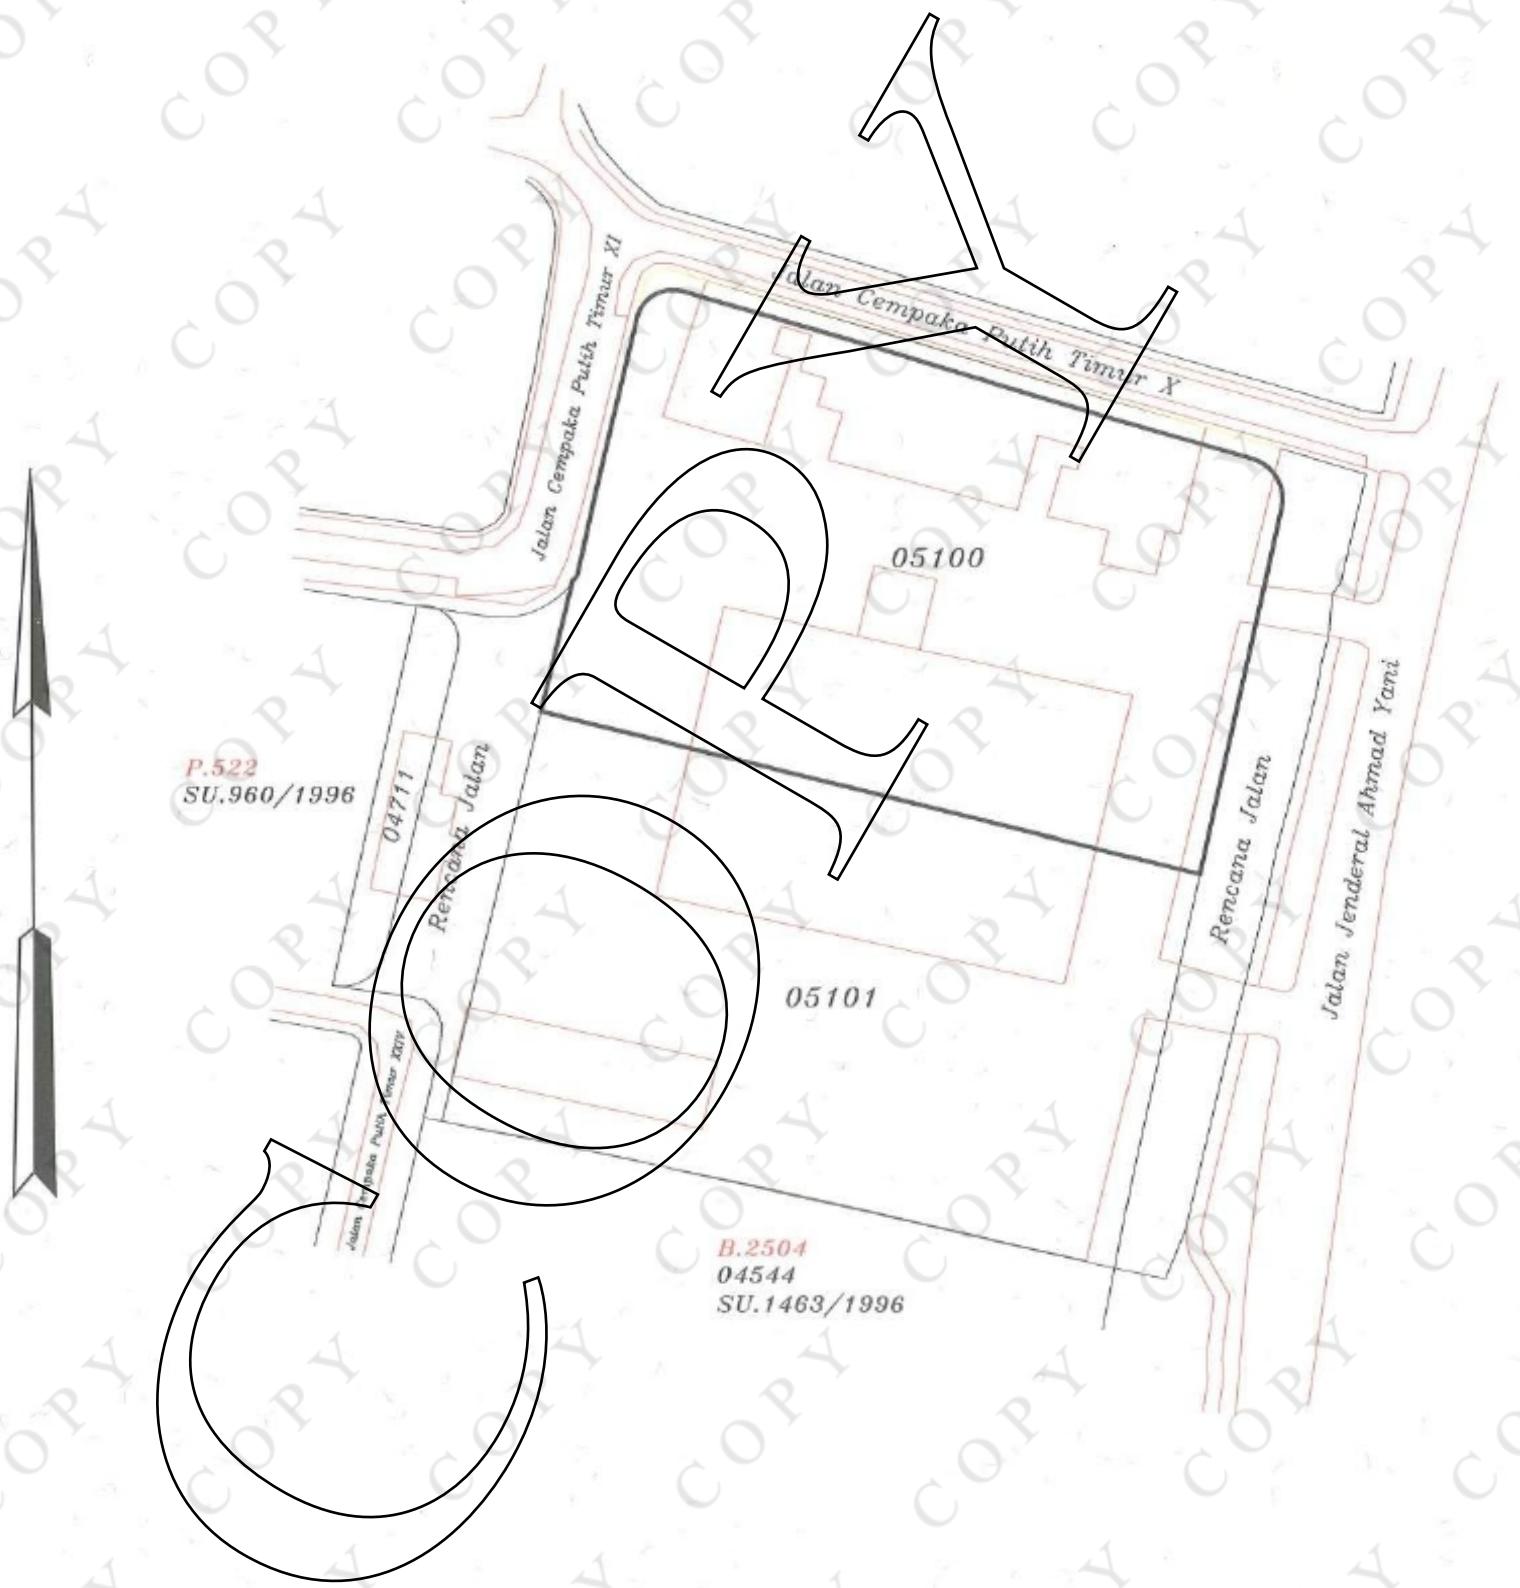

PENJELASAN : batas tanah ini

Hal lain - lain : Pecahan dari Surat Ukur tanggal . 11-10-2013 No. 00112/Cempaka Putih Timur/2013.

dari tanah Hak Guna Bangunan No. 3510/Cempaka Putih Timur.

Daftar Isian 302 tgl.

19 Januari 2017

No.

129 / 2017

Daftar Isian 307 tgl.

09 Februari 2017

No.

4748 / 2017

Tanggal Penomoran Surat Ukur

JAKARTA, 09 Februari 2017

UNTUK SERTIPIKAT

Jakarta,

13-02-2017

Kepala Seksi Survey, Pengukuran dan Pemetaan

A/n. Kepala Kantor Pertanahan

- Kabupaten / Kota

Administrasi Jakarta Pusat

Kepala Seksi Hak Tanah dan Pendaftaran Tanah

Ub. Kepala Sub Seksi Pendaftaran Hak

Kantor Pertanahan

Kabupaten / Kota

Administrasi Jakarta Pusat

ttd

ARIANTO KAL TANAH SH

NIP 19631222 198609 1 001

B. WIJANARKO, A.Ptnh., MM.

NIP 19690904 198903 1 001

Lihat surat ukur

Pemisahan

Pengabungan

Pengganti

Nomor hak :

Dilebarkan surat ukur

Tanggal Nomor

L u a s

Nomor hak

Sisa luas

Tanggal	Nomor	L u a s	Nomor hak	Sisa luas

Sisanya diuraikan dalam surat ukur Nomor :

Nomor hak :

Hal. 8 dari 8